
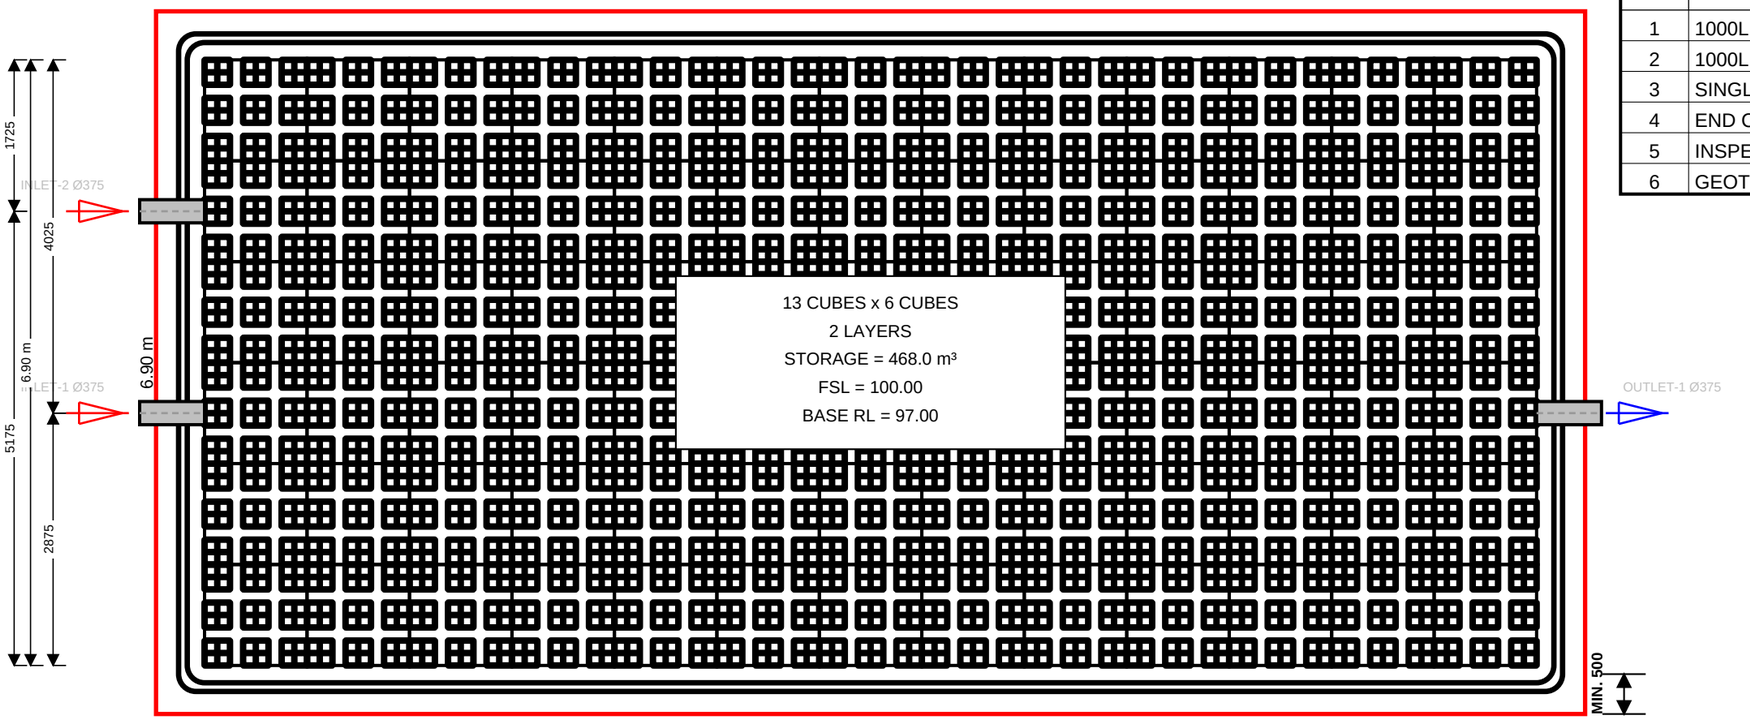


PLAN VIEW

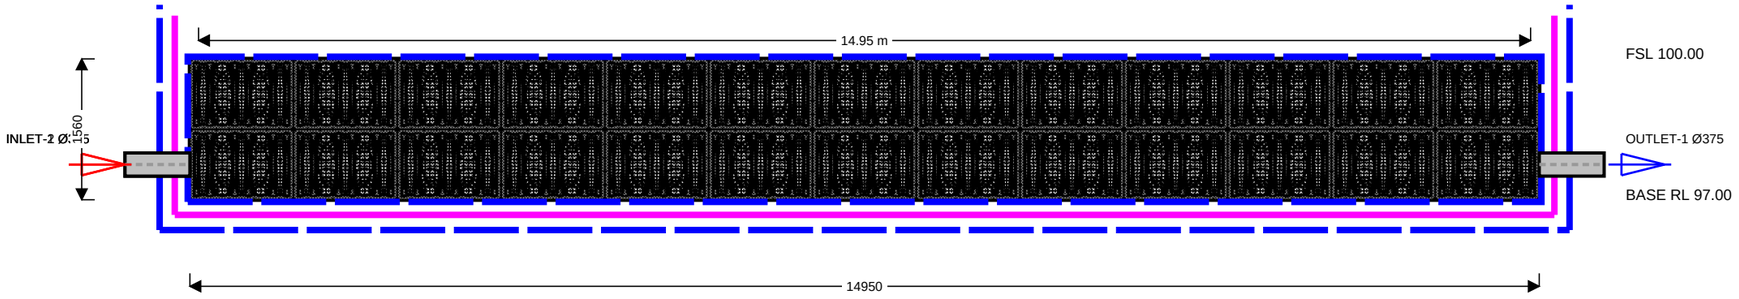

FRONT ELEVATION

PARTS LIST			
ITEM	DESCRIPTION	QTY	REMARKS
1	1000L MODULE - FULL CUBE	156	
2	1000L MODULE - SIDE PANEL FULL HEI	48	
3	SINGLE CONNECTOR	360	
4	END CAP	24	
5	INSPECTION RISER	2	
6	GEOTEXTILE WRAP	1	m²

Site Level Confirmation

Finished Surface Level (FSL)	RL:
Access Cover Thickness	mm
Inlet Invert Level	RL:
Outlet Invert Level	RL:
Company:	
Name:	
Date:	

TOLERANCE: All Dimensions to Closest 10 mm & +/- 30 mm

ALL INTERCONNECTING PIPEWORK, PITS AND ASSOCIATED DRAINAGE BY OTHERS

REV	DATE	BY	DESCRIPTION	CHK
1	21/01/2026	R.R.	INITIAL RELEASE	

CLIENT:

CONFIDENTIAL - The drawings must not be disclosed to any third parties without written permission from ATLAN STORMWATER . Unauthorised disclosure may result in prosecution.
© ATLAN STORMWATER - This drawing is the property of ATLAN STORMWATER ABN: 83 151 832 629 and is subject to return on demand. It is submitted for the use only in connection with the proposal and contracts of ATLAN STORMWATER with the expressed conditions that it is not to be reproduced or copied in any form. This data must only be used in accordance with our standard terms and conditions.
© Copyright
ATLAN STORMWATER accepts no responsibility for any loss or damage resulting from any person acting on this information.
The details and dimensions contained in this document may change, please check with ATLAN STORMWATER for confirmation of current specifications.

Drawn R.R.	Date
Check	Date
Verified	Date
Approved	Date
Request No. RN235218	

Atlan® STORMWATER


PROJECT : SAMPLE DOUBLE STACK PROJECT

TITLE

ATLAN CUBE
ATLAN CUBE 1000L MODULE (DOUBLE STACK)
6-CUBES WIDE x 13-CUBES LONG - 468m3

SCALE	SIZE	SHEET	REV
N.T.S	A3	1 OF 7	1

CUSTOMER CODE	DWG No.
24-42152	42152.P.01.10.GA

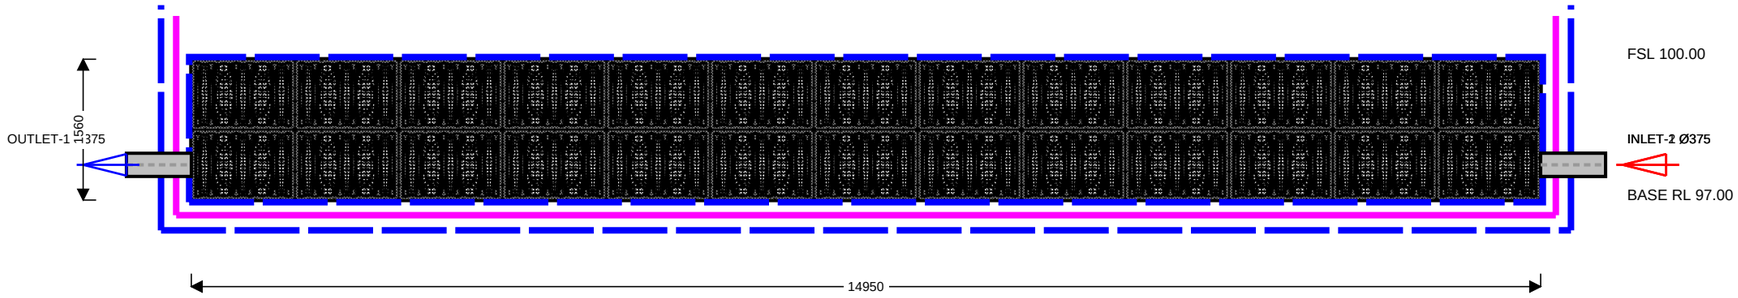

BACK ELEVATION

TOLERANCE: All Dimensions to Closest 10 mm & +/- 30 mm

ALL INTERCONNECTING PIPEWORK, PITS AND ASSOCIATED DRAINAGE BY OTHERS

REV	DATE	BY	DESCRIPTION	CHK
1	21/01/2026	R.R.	INITIAL RELEASE	

CLIENT:

CONFIDENTIAL - The drawings must not be disclosed to any third parties without written permission from ATLAN STORMWATER . Unauthorised disclosure may result in prosecution.
© ATLAN STORMWATER - This drawing is the property of ATLAN STORMWATER ABN: 83 151 832 629 and is subject to return on demand. It is submitted for the use only in connection with the proposal and contracts of ATLAN STORMWATER with the expressed conditions that it is not to be reproduced or copied in any form. This data must only be used in accordance with our standard terms and conditions.
© Copyright
ATLAN STORMWATER accepts no responsibility for any loss or damage resulting from any person acting on this information.
The details and dimensions contained in this document may change, please check with ATLAN STORMWATER for confirmation of current specifications.

Drawn R.R.	Date
Check	Date
Verified	Date
Approved	Date

Request No. RN235218

Atlan® STORMWATER

PROJECT : SAMPLE DOUBLE STACK PROJECT


TITLE

ATLAN CUBE
ATLAN CUBE 1000L MODULE (DOUBLE STACK)
6-CUBES WIDE x 13-CUBES LONG - 468m3

SCALE	SIZE	SHEET	REV
N.T.S	A3	2 OF 7	1

CUSTOMER CODE 24-42152

DWG No. 42152.P.01.10.GA

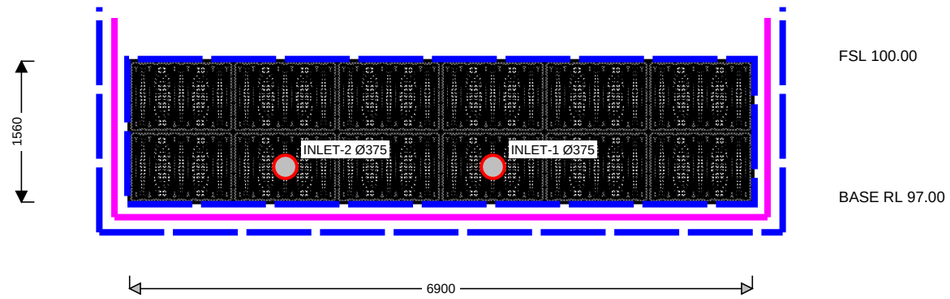

LEFT ELEVATION

TOLERANCE: All Dimensions to Closest 10 mm & +/- 30 mm

ALL INTERCONNECTING PIPEWORK, PITS AND ASSOCIATED DRAINAGE BY OTHERS

REV	DATE	BY	DESCRIPTION	CHK
1	21/01/2026	R.R.	INITIAL RELEASE	

CLIENT:

CONFIDENTIAL - The drawings must not be disclosed to any third parties without written permission from ATLAN STORMWATER . Unauthorised disclosure may result in prosecution.
© ATLAN STORMWATER - This drawing is the property of ATLAN STORMWATER ABN: 83 151 832 629 and is subject to return on demand. It is submitted for the use only in connection with the proposal and contracts of ATLAN STORMWATER with the expressed conditions that it is not to be reproduced or copied in any form. This data must only be used in accordance with our standard terms and conditions.
© Copyright
ATLAN STORMWATER accepts no responsibility for any loss or damage resulting from any person acting on this information.
The details and dimensions contained in this document may change, please check with ATLAN STORMWATER for confirmation of current specifications.

Drawn R.R.	Date
Check	Date
Verified	Date
Approved	Date

Request No.
RN235218

Atlan® STORMWATER

PROJECT : SAMPLE DOUBLE STACK PROJECT


TITLE

ATLAN CUBE
ATLAN CUBE 1000L MODULE (DOUBLE STACK)
6-CUBES WIDE x 13-CUBES LONG - 468m3

SCALE	SIZE	SHEET	REV
N.T.S	A3	3 OF 7	1

CUSTOMER CODE 24-42152

DWG No. 42152.P.01.10.GA

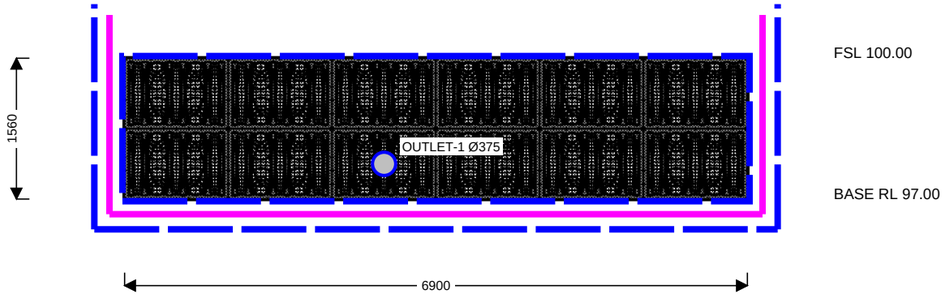

RIGHT ELEVATION

TOLERANCE: All Dimensions to Closest 10 mm & +/- 30 mm

ALL INTERCONNECTING PIPEWORK, PITS AND ASSOCIATED DRAINAGE BY OTHERS

REV	DATE	BY	DESCRIPTION	CHK
1	21/01/2026	R.R.	INITIAL RELEASE	

CLIENT:

CONFIDENTIAL - The drawings must not be disclosed to any third parties without written permission from ATLAN STORMWATER . Unauthorised disclosure may result in prosecution.
© ATLAN STORMWATER - This drawing is the property of ATLAN STORMWATER ABN: 83 151 832 629 and is subject to return on demand. It is submitted for the use only in connection with the proposal and contracts of ATLAN STORMWATER with the expressed conditions that it is not to be reproduced or copied in any form. This data must only be used in accordance with our standard terms and conditions.
© Copyright
ATLAN STORMWATER accepts no responsibility for any loss or damage resulting from any person acting on this information.
The details and dimensions contained in this document may change, please check with ATLAN STORMWATER for confirmation of current specifications.

Drawn R.R.	Date
Check	Date
Verified	Date
Approved	Date
Request No. RN235218	

Atlan® STORMWATER

PROJECT : SAMPLE DOUBLE STACK PROJECT


TITLE

ATLAN CUBE
ATLAN CUBE 1000L MODULE (DOUBLE STACK)
6-CUBES WIDE x 13-CUBES LONG - 468m3

SCALE	SIZE	SHEET	REV
N.T.S	A3	4 OF 7	1

CUSTOMER CODE 24-42152

DWG No. 42152.P.01.10.GA

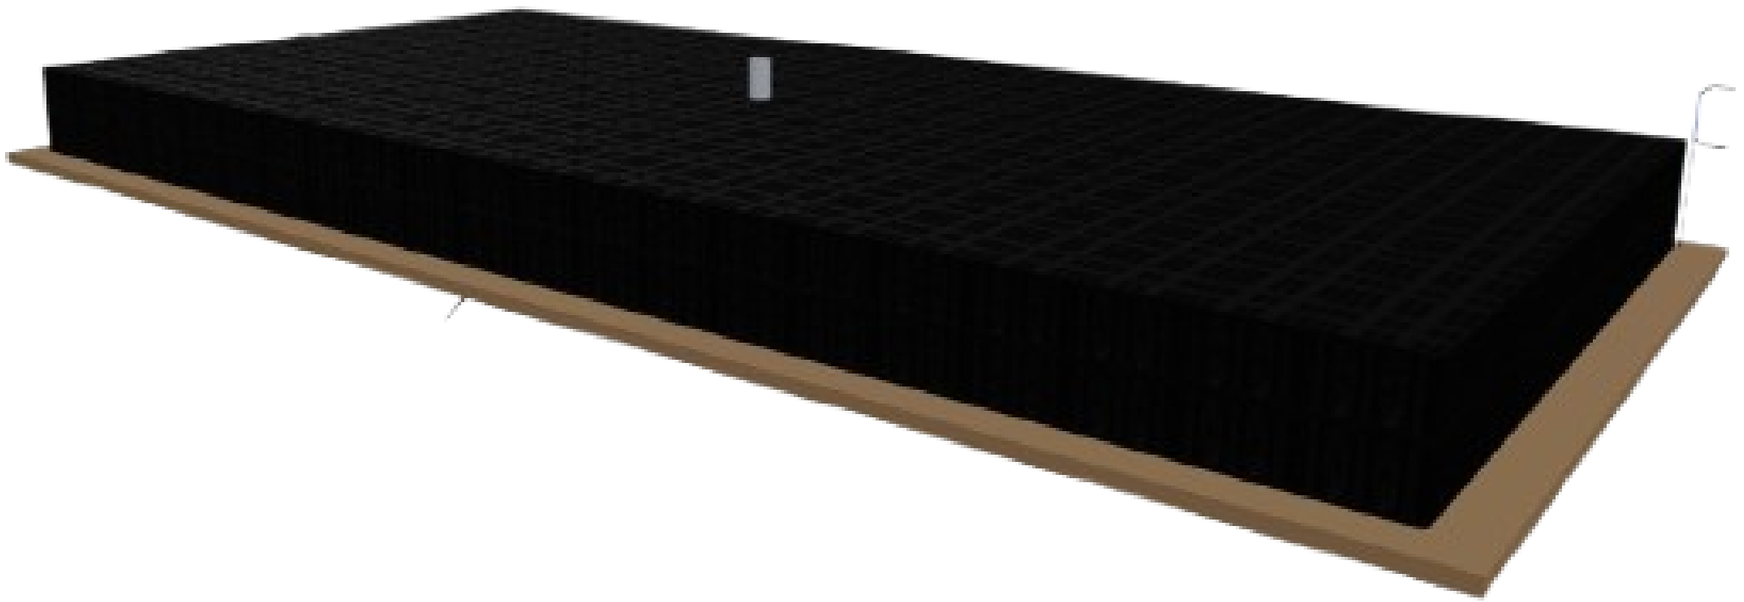

TOLERANCE: All Dimensions to Closest 10 mm & +/- 30 mm

ALL INTERCONNECTING PIPEWORK, PITS AND ASSOCIATED DRAINAGE BY OTHERS

REV	DATE	BY	DESCRIPTION	CHK
1	21/01/2026	R.R.	INITIAL RELEASE	

CLIENT:

CONFIDENTIAL - The drawings must not be disclosed to any third parties without written permission from ATLAN STORMWATER . Unauthorised disclosure may result in prosecution.
© ATLAN STORMWATER - This drawing is the property of ATLAN STORMWATER ABN: 83 151 832 629 and is subject to return on demand. It is submitted for the use only in connection with the proposal and contracts of ATLAN STORMWATER with the expressed conditions that it is not to be reproduced or copied in any form. This data must only be used in accordance with our standard terms and conditions.
© Copyright
ATLAN STORMWATER accepts no responsibility for any loss or damage resulting from any person acting on this information.
The details and dimensions contained in this document may change, please check with ATLAN STORMWATER for confirmation of current specifications.

Drawn R.R.	Date
Check	Date
Verified	Date
Approved	Date
Request No. RN235218	

Atlan® STORMWATER


PROJECT : SAMPLE DOUBLE STACK PROJECT

TITLE

ATLAN CUBE
ATLAN CUBE 1000L MODULE (DOUBLE STACK)
6-CUBES WIDE x 13-CUBES LONG - 468m3

SCALE	SIZE	SHEET	REV
N.T.S	A3	5 OF 7	1

CUSTOMER CODE	DWG No.
24-42152	42152.P.01.10.GA

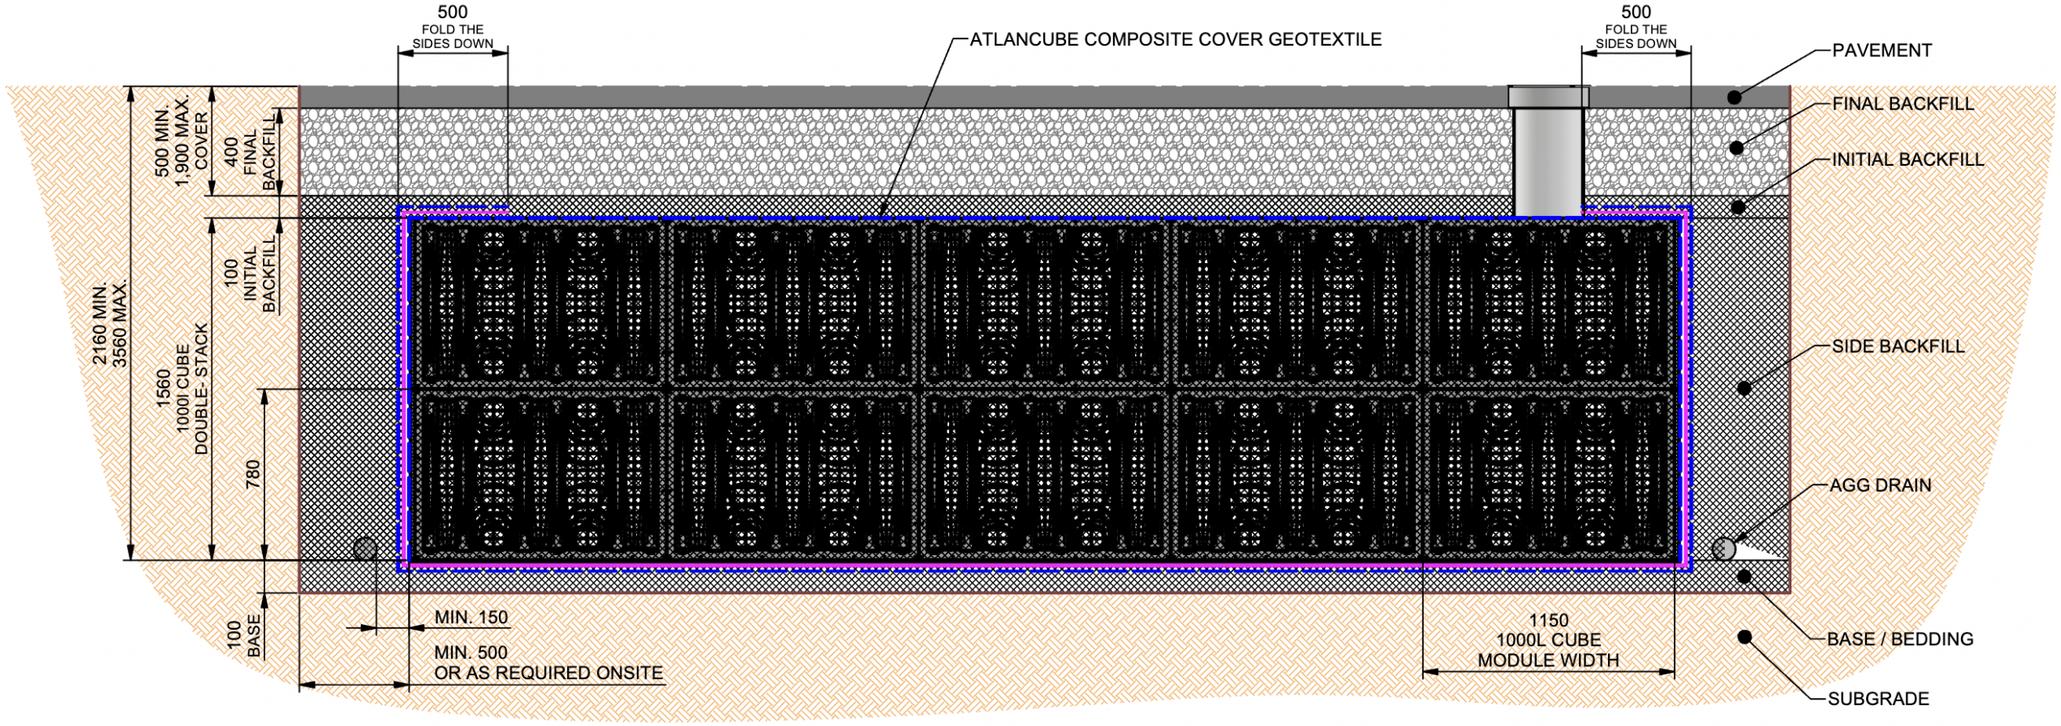

FINAL BACKFILL

Depth: 500mm minimum
Compaction: To 95% MDD minimum - Compact in 100mm layers
Material Shape: Angular
Size: Not larger than 20mm diameter
Consistency: Free of lumps, debris and sharp objects that could puncture the geotextile
Applicability: Stone, road-base or compacted granular material (non-cohesive) is acceptable if it meets these requirements. In NO case shall clays/cohesive soils be used. Ensure that any site specifications are considered for pavement make-up

INITIAL BACKFILL

Depth: 100mm
Compaction: 300kg Walk Behind Reversible Compactor
Material Shape: Sand or crushed rock
Size: Not larger than 20mm diameter
Consistency: Free of lumps, debris and sharp objects that could puncture the geotextile
Applicability: Clean washed Sand with no clay or foreign particles. In NO case shall clays/cohesive soils be used

SIDES BACKFILL

Width: 500-600mm (each side) or as required onsite
Compaction: To 95% MDD minimum - Compact in layers
Material Shape: Angular
Size: Not larger than 20mm diameter
Consistency: Free of lumps, debris and sharp objects that could puncture the geotextile
Applicability: Stone or sand is acceptable if it meets these requirements. In NO case shall clays/cohesive soils be used

BASE / BEDDING

Depth: 50mm-100mm
Compaction: To 95% MDD minimum
Material Shape: Angular
Size: Not larger than 20mm diameter
Consistency: Free of lumps, debris and sharp objects that could puncture the geotextile
Applicability: Stone or sand is acceptable if it meets these requirements. In NO case shall clays/cohesive soils be used

SUBGRADE

Compaction: To 100kPa

TOLERANCE: All Dimensions to Closest 10 mm & +/- 30 mm

ALL INTERCONNECTING PIPEWORK, PITS AND ASSOCIATED DRAINAGE BY OTHERS

REV	DATE	BY	DESCRIPTION	CHK
1	21/01/2026	R.R.	INITIAL RELEASE	

CLIENT:

CONFIDENTIAL - The drawings must not be disclosed to any third parties without written permission from ATLAN STORMWATER . Unauthorised disclosure may result in prosecution.
© ATLAN STORMWATER - This drawing is the property of ATLAN STORMWATER ABN: 83 151 832 629 and is subject to return on demand. It is submitted for the use only in connection with the proposal and contracts of ATLAN STORMWATER with the expressed conditions that it is not to be reproduced or copied in any form. This data must only be used in accordance with our standard terms and conditions.
© Copyright
ATLAN STORMWATER accepts no responsibility for any loss or damage resulting from any person acting on this information.
The details and dimensions contained in this document may change, please check with ATLAN STORMWATER for confirmation of current specifications.

Drawn R.R.	Date
Check	Date
Verified	Date
Approved	Date
Request No. RN235218	

Atlan® STORMWATER

PROJECT : SAMPLE DOUBLE STACK PROJECT

TITLE

ATLAN CUBE
ATLAN CUBE 1000L MODULE (DOUBLE STACK)
6-CUBES WIDE x 13-CUBES LONG - 468m3

SCALE	SIZE	SHEET	REV
N.T.S	A3	6 OF 7	1

CUSTOMER CODE 24-42152

DWG No. 42152.P.01.10.GA

Bill of Materials

SAMPLE DOUBLE STACK PROJECT

5 line items

View	Item	Category	Quantity	Unit
VIEW PLACEHOLDER	Atlan Cubes	Material	156	Each
VIEW PLACEHOLDER	Side Plates	Material	64	Each
VIEW PLACEHOLDER	Geotextile	Material	202.86	m2
VIEW PLACEHOLDER	Single Clip	Material	124	Each
VIEW PLACEHOLDER	Double Clip	Material	62	Each

TOLERANCE: All Dimensions to Closest 10 mm & +/- 30 mm

ALL INTERCONNECTING PIPEWORK, PITS AND ASSOCIATED DRAINAGE BY OTHERS

REV	DATE	BY	DESCRIPTION	CHK
1	21/01/2026	R.R.	INITIAL RELEASE	

CLIENT:

CONFIDENTIAL - The drawings must not be disclosed to any third parties without written permission from ATLAN STORMWATER . Unauthorised disclosure may result in prosecution.
© ATLAN STORMWATER - This drawing is the property of ATLAN STORMWATER ABN: 83 151 832 629 and is subject to return on demand. It is submitted for the use only in connection with the proposal and contracts of ATLAN STORMWATER with the expressed conditions that it is not to be reproduced or copied in any form. This data must only be used in accordance with our standard terms and conditions.
© Copyright
ATLAN STORMWATER accepts no responsibility for any loss or damage resulting from any person acting on this information.
The details and dimensions contained in this document may change, please check with ATLAN STORMWATER for confirmation of current specifications.

Drawn R.R.	Date
Check	Date
Verified	Date
Approved	Date

Request No.
RN235218

Atlan® STORMWATER

PROJECT : SAMPLE DOUBLE STACK PROJECT

TITLE

ATLAN CUBE
ATLAN CUBE 1000L MODULE (DOUBLE STACK)
6-CUBES WIDE x 13-CUBES LONG - 468m3

SCALE	SIZE	SHEET	REV
N.T.S	A3	7 OF 7	1

CUSTOMER CODE 24-42152

DWG No. 42152.P.01.10.GA